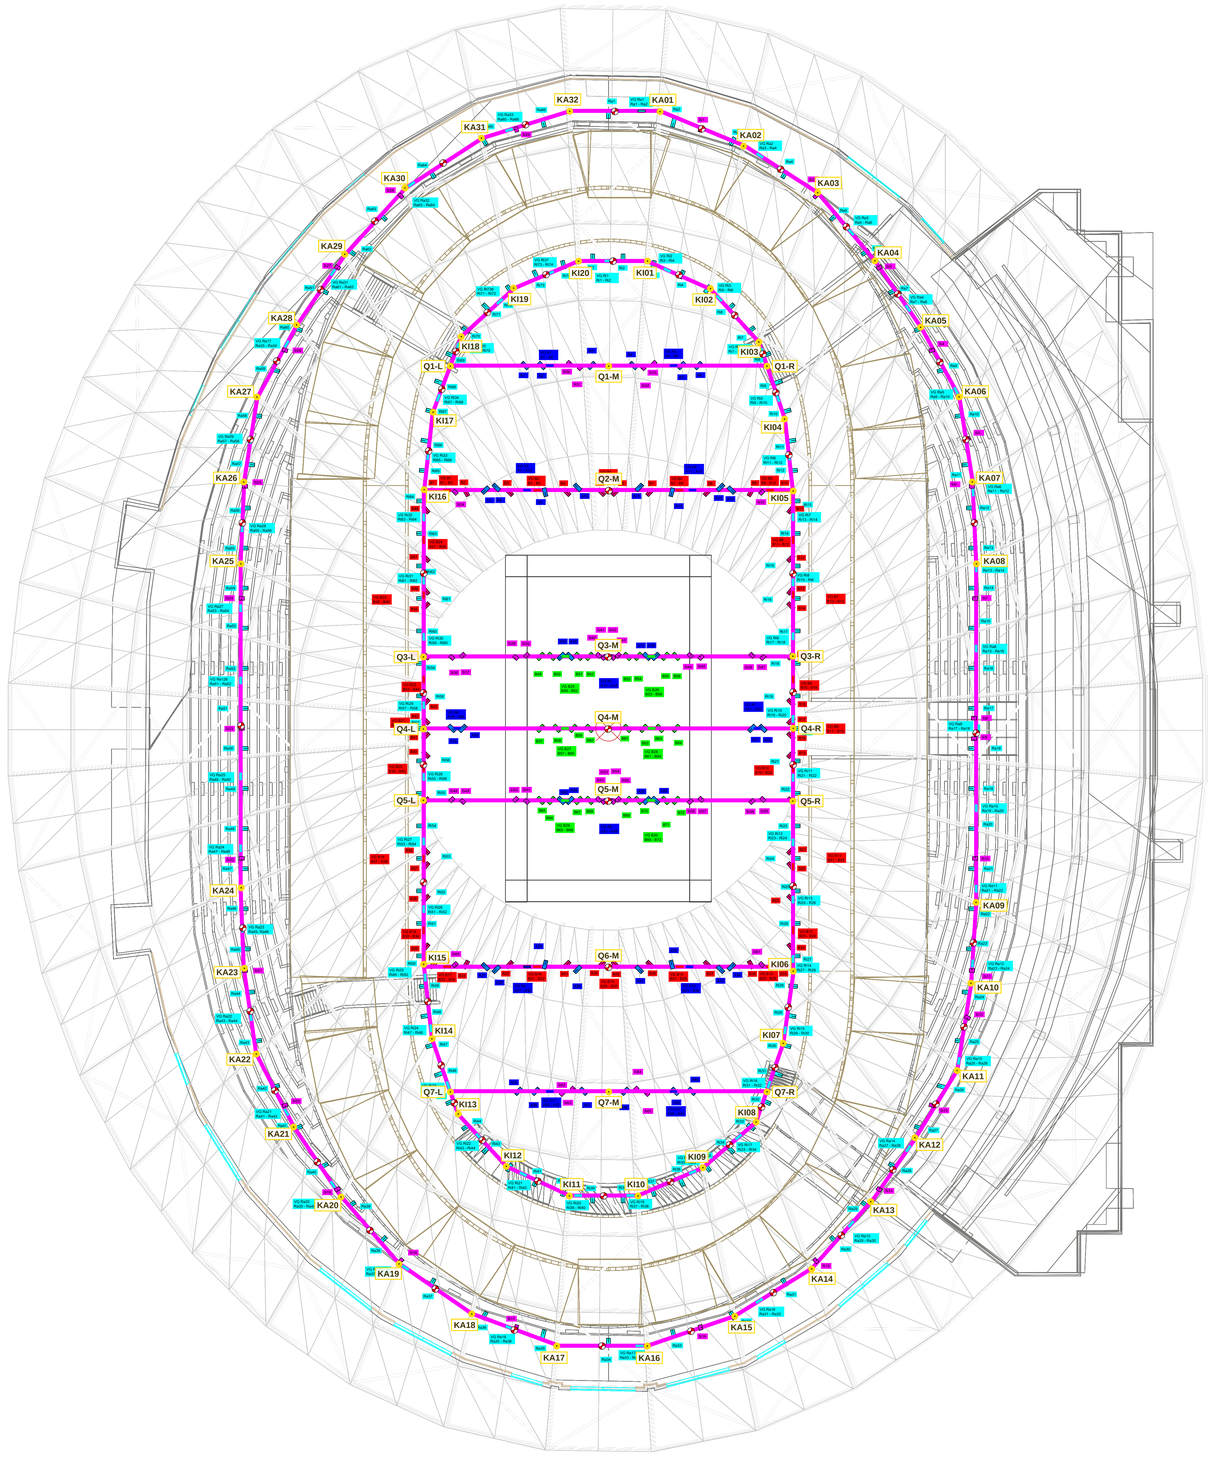


Bezeichnung Trägerpunkte

KA01 - KA32	Knickpunkt Außenring
KI01 - KI20	Knickpunkt Innenring
Qn-L / Qn-R	T-Stoß Querträger n an Innenring, links / rechts
Qn-M	Mittelpunkt Querträger n
Q1 - Q7	Querträger, von oben nach unten gezählt
	Trägerpunkt, Minipunkt = exakte Lage
	Bezugspunkt Q2-M bis Q6-M, ARnn-M, IRnn-M (Messursprung)
Blatt 2-4	Bemaßung der Fluter: Querträger (2), Außenring (3), Innenring (4)

Nummerierung im Uhrzeigersinn, Beginn an der 12-Uhr-Position.
Die Enden von Q2 und Q6 liegen auf KI05/KI16 bzw. KI06/KI15.
Maßstab dieses PDFs 1:200, abgeleitet aus dem Basketballfeld 28 x 15 m.
ARnn / IRnn: Ringabschnitte zwischen zwei gelben Punkten, im Uhrzeigersinn.

Beleuchtung

Ra1 - Ra66	LS 01 LED Fluter Sirius 1000W 5.000K
Ri1 - Ri74	LS 01 LED Fluter Sirius 1000W 5.000K
B1 - B48	LS 01.1 LED Fluter Sirius 1000W 5.700K
B48 - B72	LS 02 LED Fluter Sirius 500 5.700K
A1 - A40	LS 04 LED Fluter Sirius 500 5.000K
Si1 - Si65	LS 06 LED Fluter FL21 Mini 4.000K
VG Ra1 - VG Ra33	Vorschaltgerät LED Fluter Sirius 1000
VG Ri1 - VG Ri37	Vorschaltgerät LED Fluter Sirius 1000
VG B1 - VG B24	Vorschaltgerät LED Fluter Sirius 1000
VG B25 - VG B30	Vorschaltgerät LED Fluter Sirius 500
VG A1 - VG A12	Vorschaltgerät LED Fluter Sirius 500

Projekt:
RADSPORTZENTRUM KÖLN-MÜNGERSDORF
Peter-Günther-Weg | 50933 Köln-Müngersdorf
Gemarkung Müngersdorf | Flur 77 | Flurstücke 2205/0, 2206/0, 2207/0, 2208/0, 2210/0 tlw.

Bauherr:
Kölner Sportstätten GmbH
Aachener Straße 999 | 50933 Köln

Projektsteuerer:
moderne stadt
Brückenstraße 17 | 50667Köln | Tel: 0221-20594-33

Architekten Entwurfsplanung | Genehmigungsplanung | Ausführplanung LPH 5:
Schürmann Architekten
Schürbusch 26 | 48163 Münster | Tel. 0251-712450

Totalübernehmer:
Zech Sports GmbH
Heerdter Lohweg 35 | 40549 Düsseldorf | Tel. 0211-50664-300

Architekten Ausführungs- und Detailplanung LPH 5+:
arc | architektur concept Pfaffhausen + Kollegen
Scheringerstraße 3 |08056 Zwickau | Tel. 0375-27735-0

Ausführung Elektrotechnik:
Oertel & Prümm GmbH & Co.KG
Widdersdorferstraße 190 | 50825 Köln | Tel. 0221-546600
OERTEL & PRÜMM

Planer Beleuchtung Radbahn / Spielfläche:
Siteco GmbH
Georg-Simon-Ohm-Straße 50 | 83301 Traunreut| Tel. 08669-33-0

Planinhalt:
Grundriss Dachkonstruktion
Beleuchtung Radbahn / Spielfläche


Bearbeiter:	Leistungsphase:	Blattformat:	Maßstab:	Datum Erstellung:
TS	Montageplanung	1950 x 841	1:50	21.08.2026

Projekt:	LPH:	Fachplaner:	Plantyp:	Ebene:	Planbereich:	Blattnr:	Status:	Index:
R S Z	008	L I C	G R	D A	2.1	0 0 1	P	0 1


Blatt 2 · Bemaßung Querträger Q2 - Q6: Fluter ab Bezugspunkt Qn-M

Radsportzentrum Köln-Müngersdorf · Grundriss Dachkonstruktion · Beleuchtung Radbahn / Spielfläche · Maße in m, aus dem Grundriss (Blatt 1, 1:200) abgeleitet · Träger hier vergrößert dargestellt


Q2

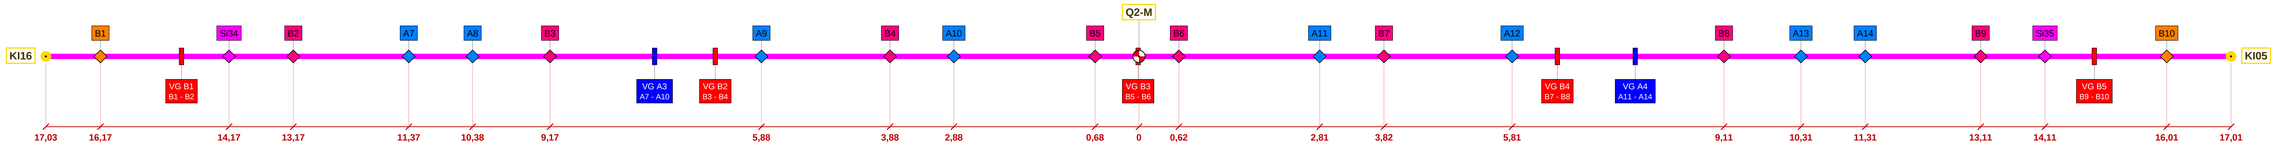


Q3

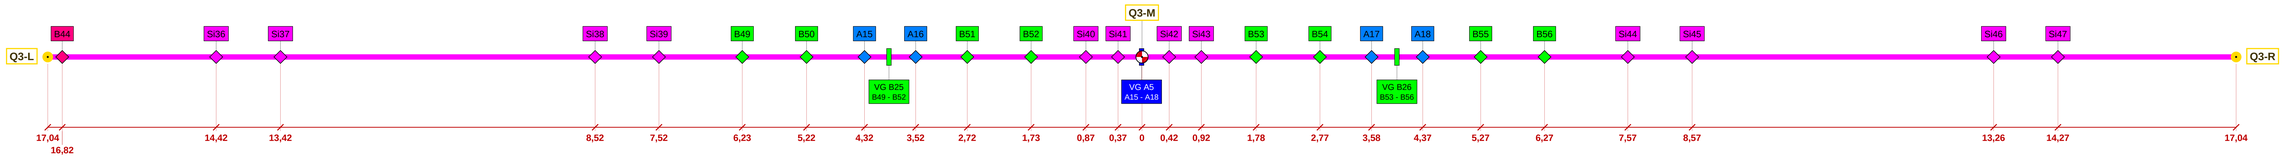


Q4

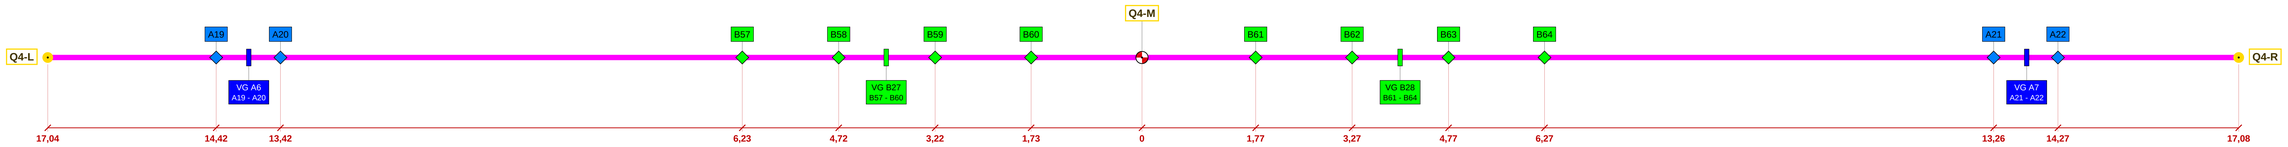

Q5

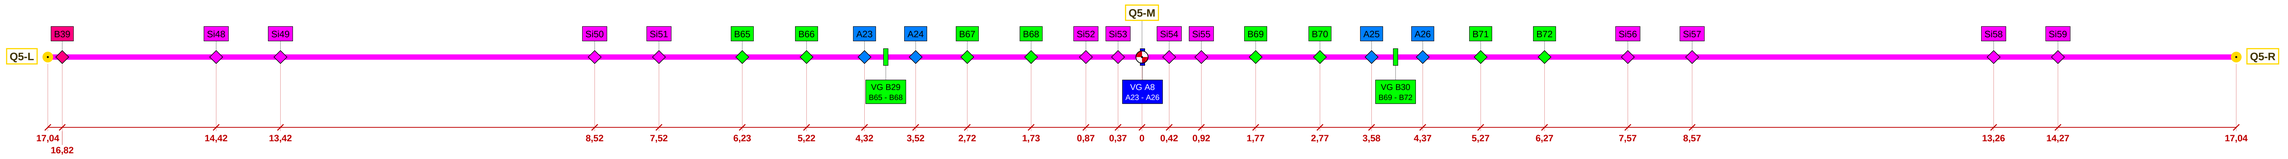

Q6

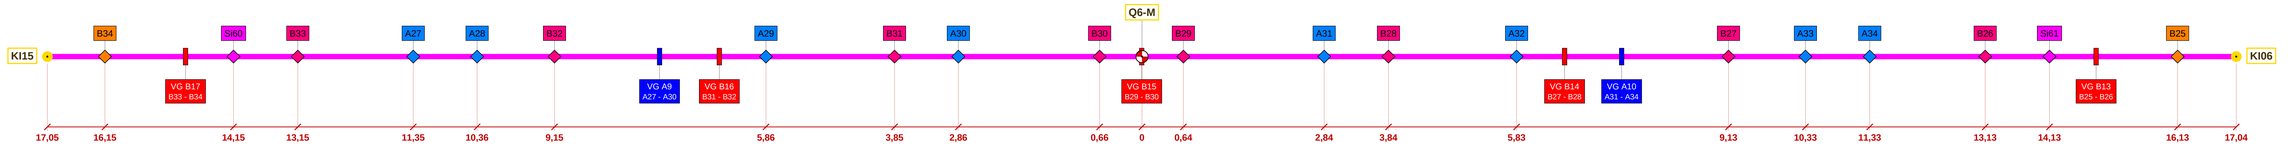


Fluter (Farbe wie Plan) · Vorschaltgerät (nur Lage) · Bezugspunkt (Messursprung) · Abschnittsende · Maße [m] ab Bezugspunkt, rot


Blatt 3 · Bemaßung Außenring AR01 - AR32: Fluter ab Bezugspunkt ARnn-M (Abschnittsmitte)

Radsportzentrum Köln-Müngersdorf · Grundriss Dachkonstruktion · Beleuchtung Radbahn / Spielfläche · Maße in m, aus dem Grundriss (Blatt 1, 1:200) abgeleitet · Träger hier vergrößert dargestellt


AR01 (KA01 - KA02, 8,33 m)

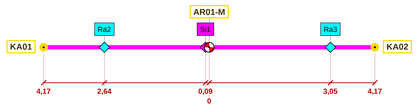


AR02 (KA02 - KA03, 8,08 m)

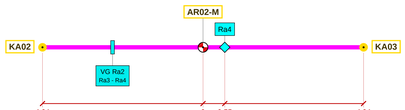

AR03 (KA03 - KA04, 8,21 m)

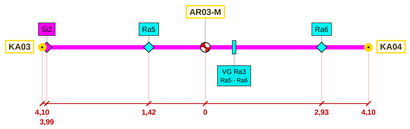


AR04 (KA04 - KA05, 7,44 m)

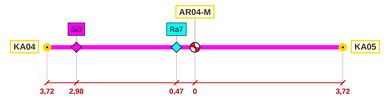


AR05 (KA05 - KA06, 7,34 m)




AR06 (KA06 - KA07, 7,94 m)

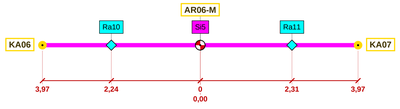

AR07 (KA07 - KA08, 7,56 m)

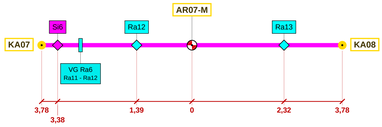

AR08 (KA08 - KA09, 31,24 m)

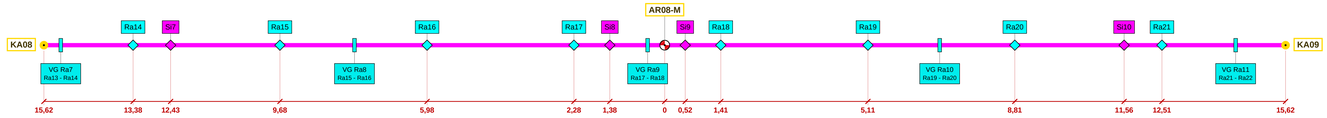


AR09 (KA09 - KA10, 7,47 m)




AR10 (KA10 - KA11, 8,16 m)



AR11 (KA11 - KA12, 7,32 m)

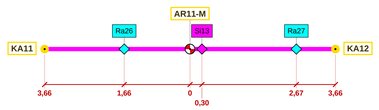

AR12 (KA12 - KA13, 7,17 m)

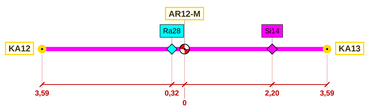

AR13 (KA13 - KA14, 8,25 m)



AR14 (KA14 - KA15, 8,34 m)

AR15 (KA15 - KA16, 8,53 m)

AR16 (KA16 - KA17, 8,35 m)

AR17 (KA17 - KA18, 8,38 m)

AR18 (KA18 - KA19, 8,15 m)

AR19 (KA19 - KA20, 8,17 m)

AR20 (KA20 - KA21, 7,79 m)

AR21 (KA21 - KA22, 7,56 m)

AR22 (KA22 - KA23, 7,99 m)

AR23 (KA23 - KA24, 7,43 m)

AR24 (KA24 - KA25, 29,89 m)

AR25 (KA25 - KA26, 7,56 m)

AR26 (KA26 - KA27, 7,93 m)

AR27 (KA27 - KA28, 7,59 m)

AR28 (KA28 - KA29, 7,88 m)

AR29 (KA29 - KA30, 8,27 m)

AR30 (KA30 - KA31, 8,42 m)

AR31 (KA31 - KA32, 8,51 m)


AR32 (KA32 - KA01, 8,33 m)

◆ Fluter (Farbe wie Plan) ▮ Vorschaltgerät (nur Lage) ◔ Bezugspunkt (Messursprung) ◉ Abschnittsende Maße [m] ab Bezugspunkt, rot


Blatt 4 · Bemaßung Innenring IR01 - IR30: Fluter ab Bezugspunkt IRnn-M (Abschnittsmitte)

Radsportzentrum Köln-Müngersdorf · Grundriss Dachkonstruktion · Beleuchtung Radbahn / Spielfläche · Maße in m, aus dem Grundriss (Blatt 1, 1:200) abgeleitet · Träger hier vergrößert dargestellt


IR01 (KI01 - KI02, 6,34 m)

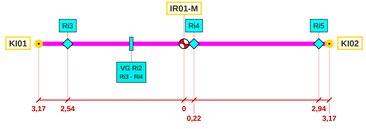

IR02 (KI02 - KI03, 6,65 m)

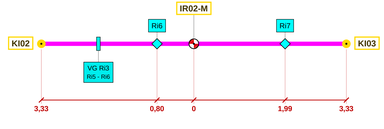


IR03 (KI03 - Q1-R, 2,35 m)

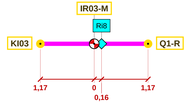


IR04 (Q1-R - KI04, 5,14 m)




IR05 (KI04 - KI05, 6,69 m)

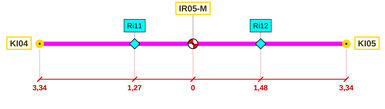


IR06 (KI05 - Q3-R, 15,25 m)

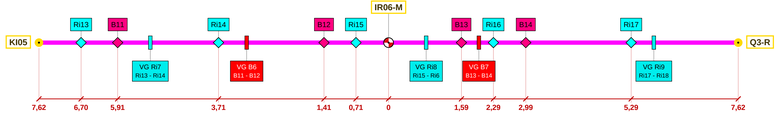

IR07 (Q3-R - Q4-R, 6,65 m)

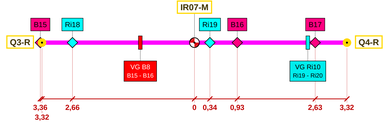


IR08 (Q4-R - Q5-R, 6,71 m)

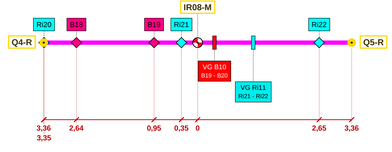

IR09 (Q5-R - KI06, 15,69 m)



IR10 (KI06 - KI07, 6,73 m)

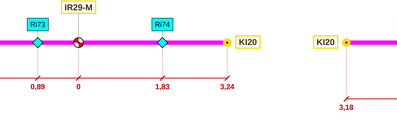

IR11 (KI07 - Q7-R, 4,72 m)



IR12 (Q7-R - KI08, 2,96 m)

IR13 (KI08 - KI09, 6,47 m)

IR14 (KI09 - KI10, 6,53 m)

IR15 (KI10 - KI11, 6,33 m)

IR16 (KI11 - KI12, 6,42 m)

IR17 (KI12 - KI13, 6,56 m)

IR18 (KI13 - Q7-L, 2,16 m)

IR19 (Q7-L - KI14, 5,19 m)

IR20 (KI14 - KI15, 6,92 m)

IR21 (KI15 - Q5-L, 15,13 m)

IR22 (Q5-L - Q4-L, 6,58 m)

IR23 (Q4-L - Q3-L, 6,65 m)

IR24 (Q3-L - KI16, 15,44 m)

IR25 (KI16 - KI17, 7,20 m)

IR26 (KI17 - Q1-L, 4,54 m)

IR27 (Q1-L - KI18, 2,90 m)

IR28 (KI18 - KI19, 6,58 m)

IR29 (KI19 - KI20, 6,49 m)

IR30 (KI20 - KI01, 6,36 m)

◆ Fluter (Farbe wie Plan) ▮ Vorschaltgerät (nur Lage) ◐ Bezugspunkt (Messursprung) ● Abschnittsende Maße [m] ab Bezugspunkt, rot