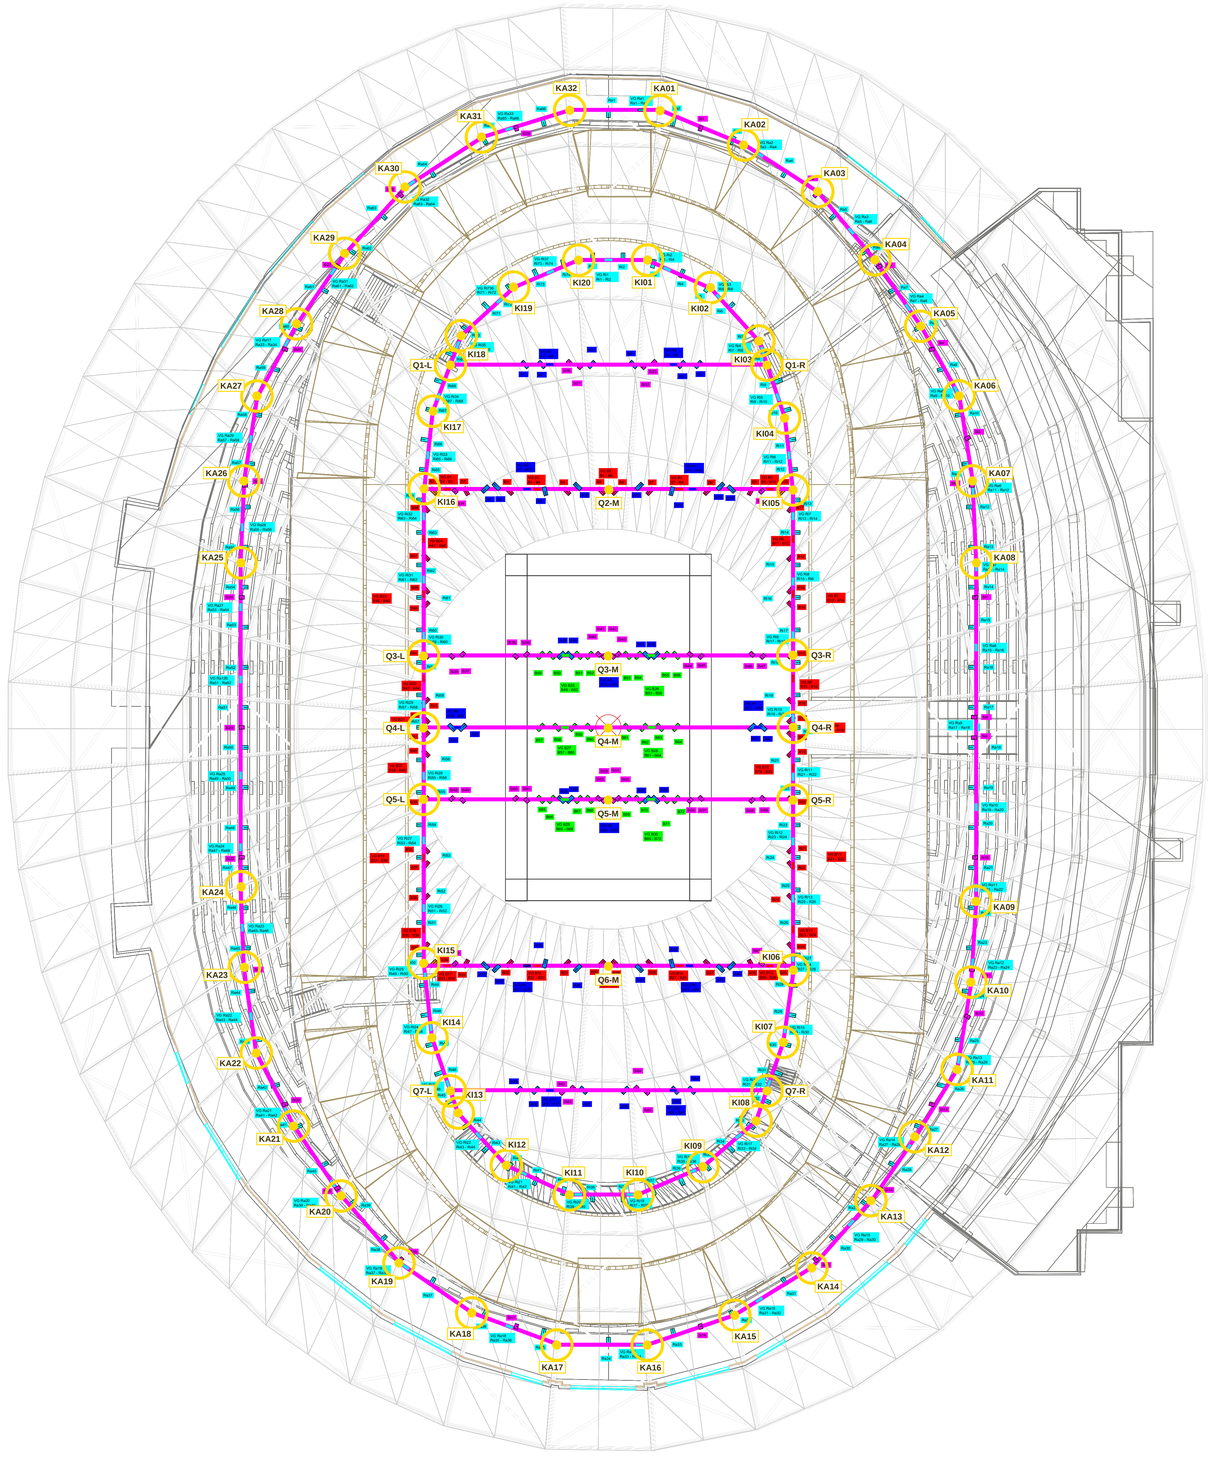



**Bezeichnung Trägerpunkte**

| | |
|---|---|
| **KA01 - KA32** | Knickpunkt Außenring |
| **KI01 - KI20** | Knickpunkt Innenring |
| **Qn-L / Qn-R** | T-Stoß Querträger n an Innenring, links / rechts |
| **Qn-M** | Mittelpunkt Querträger n |
| **Q1 - Q7** | Querträger, von oben nach unten gezählt |
| | Knickpunkt / T-Stoß |
| | Mittelpunkt Querträger |

Nummerierung im Uhrzeigersinn, Beginn an der 12-Uhr-Position.
Die Enden von Q2 und Q6 liegen auf KI05/KI16 bzw. KI06/KI15.

## Beleuchtung

| | |
|---|---|
| Ra1 - Ra66 | LS 01<br>LED Fluter Sirius 1000W<br>5.000K |
| Ri1 - Ri74 | LS 01<br>LED Fluter Sirius 1000W<br>5.000K |
| B1 - B48 | LS 01.1<br>LED Fluter Sirius 1000W<br>5.700K |
| B48 - B72 | LS 02<br>LED Fluter Sirius 500<br>5.700K |
| A1 - A40 | LS 04<br>LED Fluter Sirius 500<br>5.000K |
| Si1 - Si65 | LS 06<br>LED Fluter FL21 Mini<br>4.000K |
| VG Ra1 - VG Ra33 | Vorschaltgerät<br>LED Fluter Sirius 1000 |
| VG Ri1 - VG Ri37 | Vorschaltgerät<br>LED Fluter Sirius 1000 |
| VG B1 - VG B24 | Vorschaltgerät<br>LED Fluter Sirius 1000 |
| VG B25 - VG B30 | Vorschaltgerät<br>LED Fluter Sirius 500 |
| VG A1 - VG A12 | Vorschaltgerät<br>LED Fluter Sirius 500 |

Projekt:
**RADSPORTZENTRUM KÖLN-MÜNGERSDORF**
**Peter-Günther-Weg | 50933 Köln-Mungersdorf**
Gemarkung Müngersdorf | Flur 77 | Flurstücke 2205/0, 2206/0, 2207/0, 2208/0, 2210/0 tlw.

Bauherr:
**Kölner Sportstätten GmbH**
Aachener Straße 999 | 50933 Köln

Projektsteuerer:
**moderne stadt**
Brückenstraße 17 | 50667Köln | Tel: 0221-20594-33

Architekten Entwurfsplanung | Genehmigungsplanung | Ausführplanung LPH 5:
**Schürmann Architekten**
Schürbusch 26 | 48163 Münster | Tel. 0251-712450

Totalübernehmer:
**Zech Sports GmbH**
Heerdter Lohweg 35 | 40549 Düsseldorf | Tel. 0211-50664-300

Architekten Ausführungs- und Detailplanung LPH 5+:
**arc | architektur concept Pfaffhausen + Kollegen**
Scheringerstraße 3 |08056 Zwickau | Tel. 0375-27735-0

Ausführung Elektrotechnik:
**Oertel & Prümm GmbH & Co.KG**
Widdersdorferstraße 190 | 50825 Köln | Tel. 0221-546600
OERTEL & PRÜMM

Planer Beleuchtung Radbahn / Spielfläche:
**Siteco GmbH**
Georg-Simon-Ohm-Straße 50 | 83301 Traunreut| Tel. 08669-33-0

Planinhalt:
**Grundriss Dachkonstruktion**
**Beleuchtung Radbahn / Spielfläche**

| Bearbeiter: | Leistungsphase: | Blattformat: | Maßstab: | Datum Erstellung: |
|---|---|---|---|---|
| TS | Montageplanung | 1950 x 841 | 1:50 | 21.08.2026 |

| Projekt: | LPH: | Fachplaner: | Plantyp: | Ebene: | Planbereich: | Blattnr: | Status: | Index: |
|---|---|---|---|---|---|---|---|---|
| R S Z | 008 | L I C | G R | D A | 2.1 | 0 0 1 | P | 0 1 |