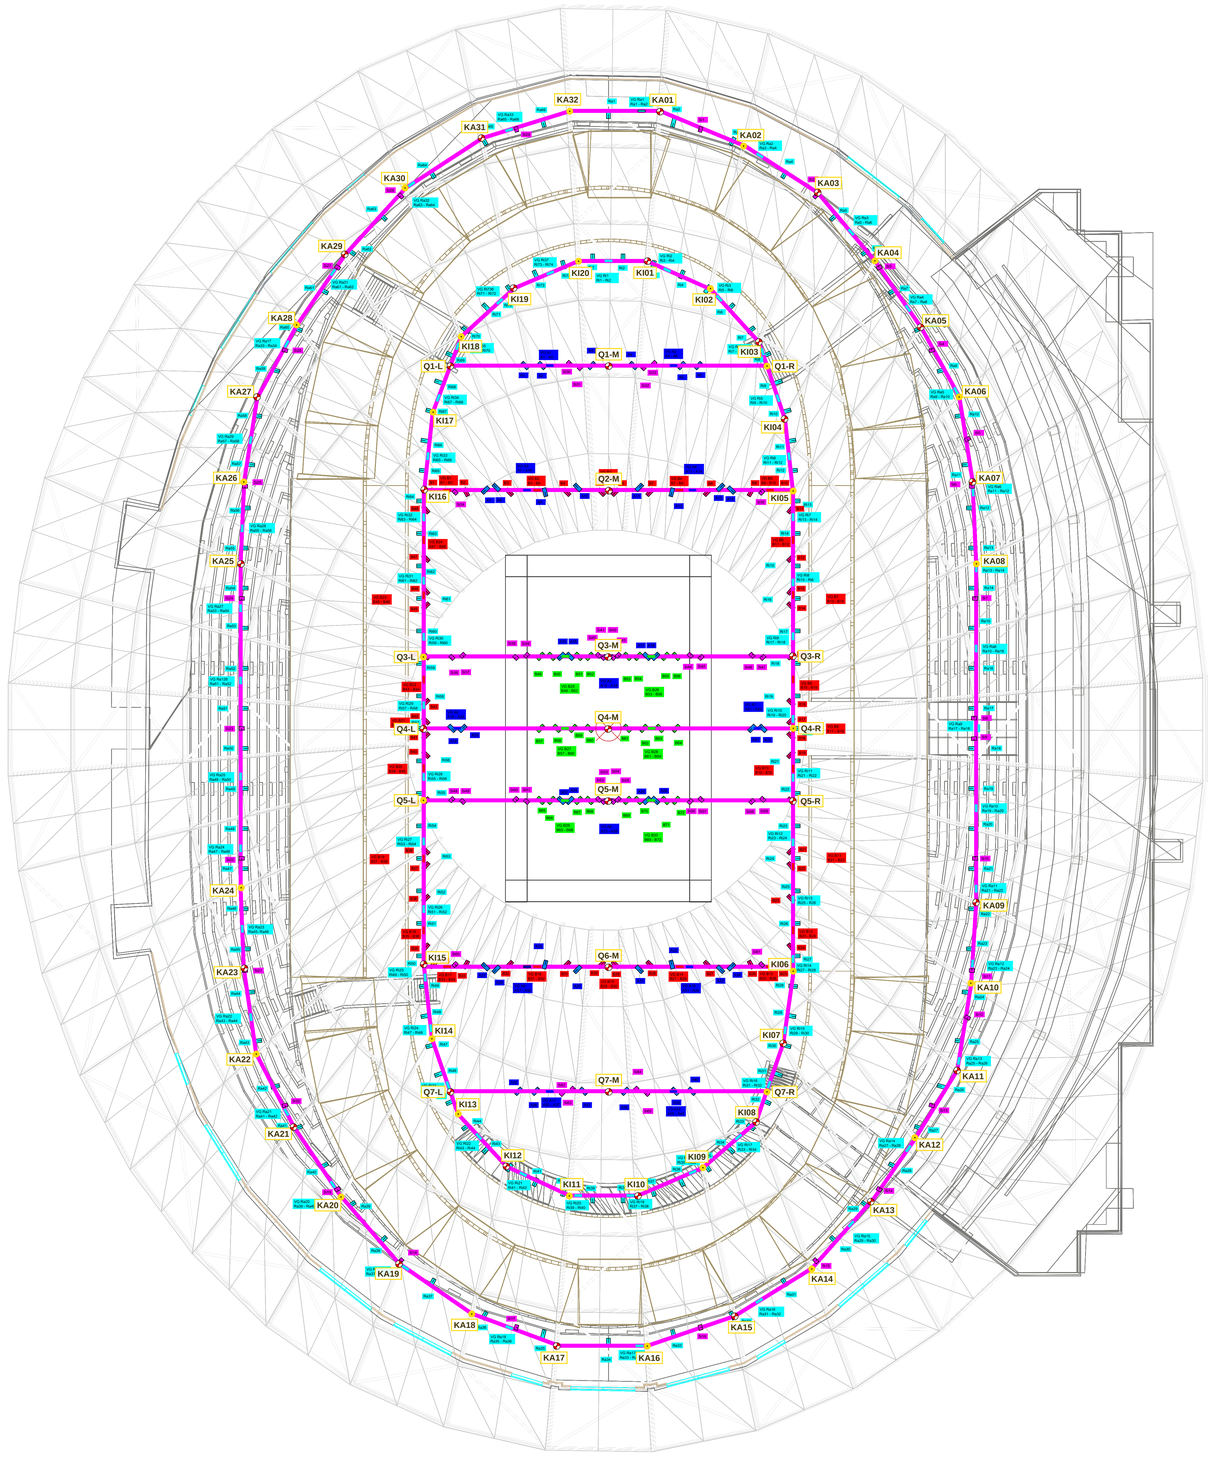


Bezeichnung Trägerpunkte

KA01 - KA32	Knickpunkt Außenring
KI01 - KI20	Knickpunkt Innenring
Qn-L / Qn-R	T-Stoß Querträger n an Innenring, links / rechts
Qn-M	Mittelpunkt Querträger n
Q1 - Q7	Querträger, von oben nach unten gezählt
	Trägerpunkt, Minipunkt = exakte Lage
	Bezugspunkt: Q1-M bis Q7-M und jeder zweite Ringpunkt ab KA01 bzw. KI01
Blatt 2-4	Bemaßung der Fluter: Querträger (2), Außenring (3), Innenring (4)

Nummerierung im Uhrzeigersinn, Beginn an der 12-Uhr-Position.
Die Enden von Q2 und Q6 liegen auf KI05/KI16 bzw. KI06/KI15.
Maßstab dieses PDFs 1:200, abgeleitet aus dem Basketballfeld 28 x 15 m.
Ringe: Bezugspunkt und gelber Punkt wechseln sich ab, gemessen wird beidseitig bis zum nächsten gelben Punkt.

Beleuchtung

Ra1 - Ra66	LS 01 LED Fluter Sirius 1000W 5.000K
Ri1 - Ri74	LS 01 LED Fluter Sirius 1000W 5.000K
B1 - B48	LS 01.1 LED Fluter Sirius 1000W 5.700K
B48 - B72	LS 02 LED Fluter Sirius 500 5.700K
A1 - A40	LS 04 LED Fluter Sirius 500 5.000K
Si1 - Si65	LS 06 LED Fluter FL21 Mini 4.000K
VG Ra1 - VG Ra33	Vorschaltgerät LED Fluter Sirius 1000
VG Ri1 - VG Ri37	Vorschaltgerät LED Fluter Sirius 1000
VG B1 - VG B24	Vorschaltgerät LED Fluter Sirius 1000
VG B25 - VG B30	Vorschaltgerät LED Fluter Sirius 500
VG A1 - VG A12	Vorschaltgerät LED Fluter Sirius 500

Projekt:
RADSPORTZENTRUM KÖLN-MÜNGERSDORF
Peter-Günther-Weg | 50933 Köln-Mungersdorf
Gemarkung Müngersdorf | Flur 77 | Flurstücke 2205/0, 2206/0, 2207/0, 2208/0, 2210/0 tlw.

Bauherr:
Kölner Sportstätten GmbH
Aachener Straße 999 | 50933 Köln

Projektsteuerer:
moderne stadt
Brückenstraße 17 | 50667Köln | Tel: 0221-20594-33

Architekten Entwurfsplanung | Genehmigungsplanung | Ausführplanung LPH 5:
Schürmann Architekten
Schürbusch 26 | 48163 Münster | Tel. 0251-712450

Totalübernehmer:
Zech Sports GmbH
Heerdter Lohweg 35 | 40549 Düsseldorf | Tel. 0211-50664-300

Architekten Ausführungs- und Detailplanung LPH 5+:
arc | architektur concept Pfaffhausen + Kollegen
Scheringerstraße 3 |08056 Zwickau | Tel. 0375-27735-0

Ausführung Elektrotechnik:
Oertel & Prümm GmbH & Co.KG
Widdersdorferstraße 190 | 50825 Köln | Tel. 0221-546600
Planer Beleuchtung Radbahn / Spielfläche:
Siteco GmbH
Georg-Simon-Ohm-Straße 50 | 83301 Traunreut| Tel. 08669-33-0

Planinhalt:
Grundriss Dachkonstruktion
Beleuchtung Radbahn / Spielfläche


Bearbeiter:	Leistungsphase:	Blattformat:	Maßstab:	Datum Erstellung:
TS	Montageplanung	1950 x 841	1:50	21.08.2026

Projekt:	LPH:	Fachplaner:	Plantyp:	Ebene:	Planbereich:	Blattnr:	Status:	Index:
R S Z	008	L I C	G R	D A	2.1	0 0 1	P	0 1

Blatt 2 · Bemaßung Querträger Q1 - Q7: Fluter ab Bezugspunkt Qn-M

Radsportzentrum Köln-Müngersdorf · Grundriss Dachkonstruktion · Beleuchtung Radbahn / Spielfläche · Maße in m, aus dem Grundriss (Blatt 1, 1:200) abgeleitet · Träger hier vergrößert dargestellt

Q1

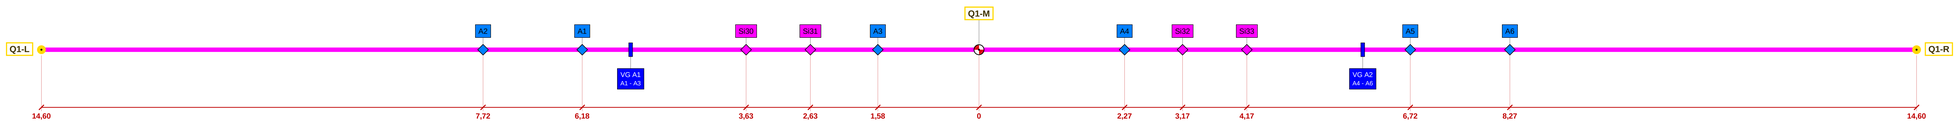


Q2




Q3



Q4

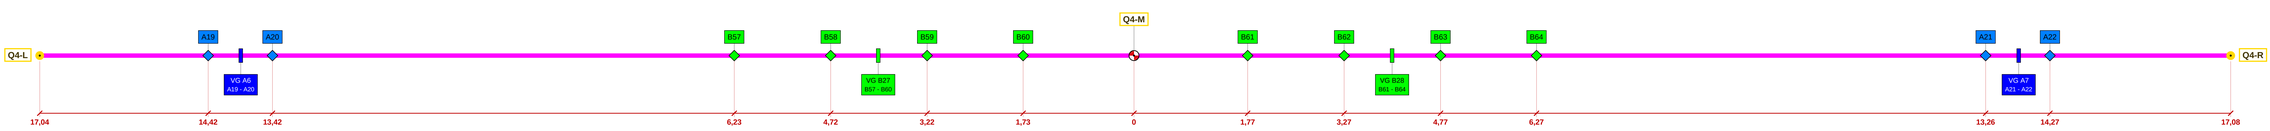


Q5

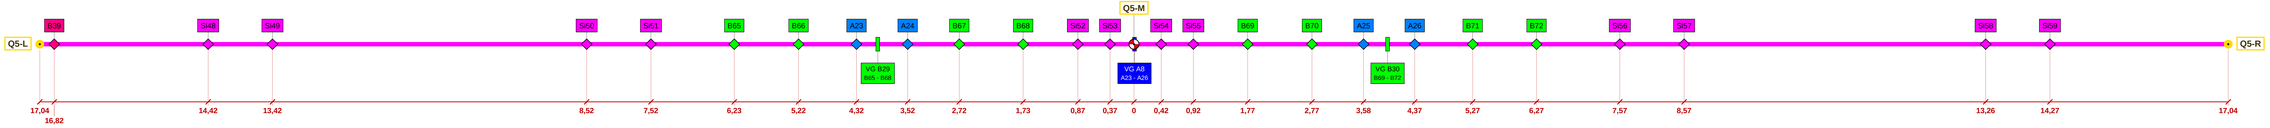

Q6



Q7

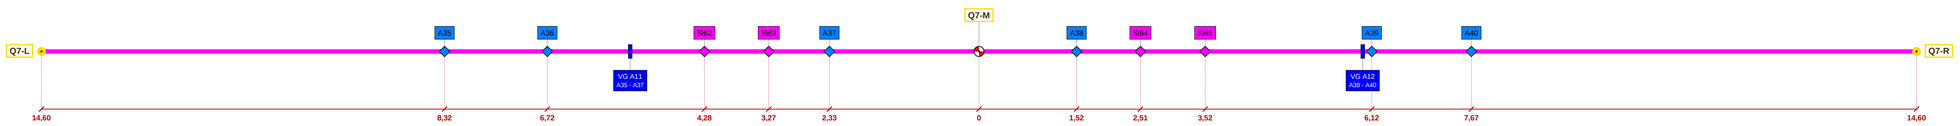


◆ Fluter (Farbe wie Plan) ▮ Vorschaltgerät (nur Lage) ◉ Bezugspunkt (Messursprung) ⊙ Abschnittsende Maße [m] ab Bezugspunkt, rot


Blatt 3 · Bemaßung Außenring: Fluter ab jedem zweiten Ringpunkt (KA01, KA03 ... KA31) bis zum nächsten gelben Punkt

Radsportzentrum Köln-Müngersdorf · Grundriss Dachkonstruktion · Beleuchtung Radbahn / Spielfläche · Maße in m, aus dem Grundriss (Blatt 1, 1:200) abgeleitet · Träger hier vergrößert dargestellt


KA32 - KA01 - KA02 (8,33 m + 8,33 m, am Bezugspunkt abgewickelt)

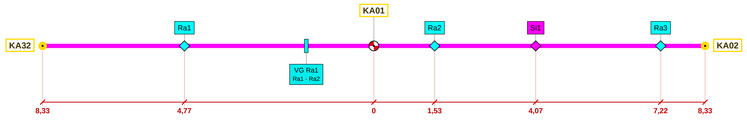


KA02 - KA03 - KA04 (8,08 m + 8,21 m, am Bezugspunkt abgewickelt)

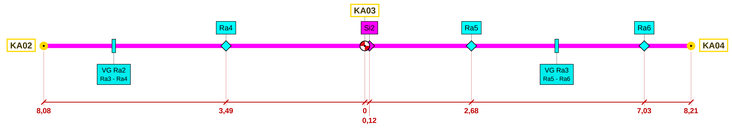


KA04 - KA05 - KA06 (7,44 m + 7,34 m, am Bezugspunkt abgewickelt)

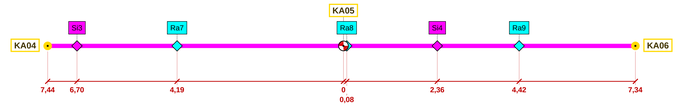

KA06 - KA07 - KA08 (7,94 m + 7,56 m, am Bezugspunkt abgewickelt)

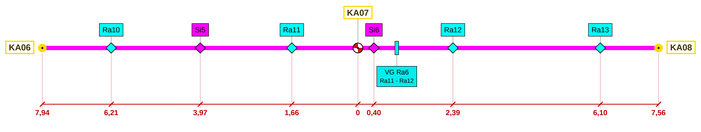

KA08 - KA09 - KA10 (31,24 m + 7,47 m, am Bezugspunkt abgewickelt)

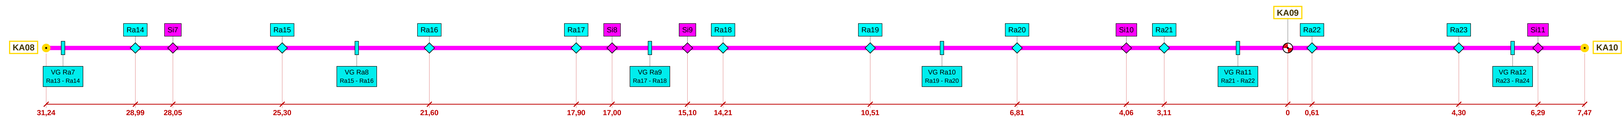

KA10 - KA11 - KA12 (8,16 m + 7,32 m, am Bezugspunkt abgewickelt)




KA12 - KA13 - KA14 (7,17 m + 8,25 m, am Bezugspunkt abgewickelt)




KA14 - KA15 - KA16 (8,34 m + 8,53 m, am Bezugspunkt abgewickelt)


KA16 - KA17 - KA18 (8,35 m + 8,38 m, am Bezugspunkt abgewickelt)

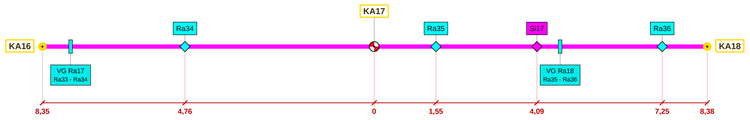


KA18 - KA19 - KA20 (8,15 m + 8,17 m, am Bezugspunkt abgewickelt)

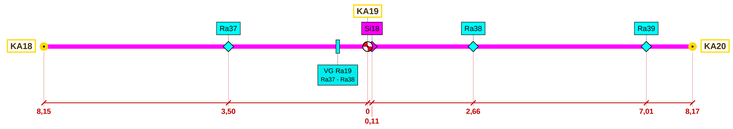


KA20 - KA21 - KA22 (7,79 m + 7,56 m, am Bezugspunkt abgewickelt)

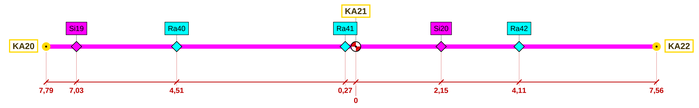


KA22 - KA23 - KA24 (7,99 m + 7,43 m, am Bezugspunkt abgewickelt)

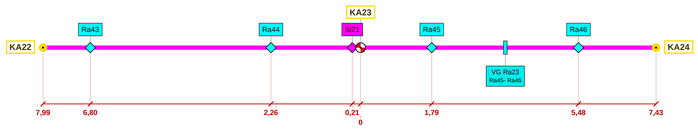


KA24 - KA25 - KA26 (29,89 m + 7,56 m, am Bezugspunkt abgewickelt)

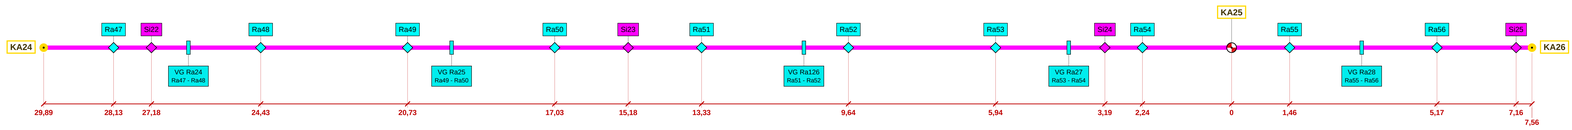


KA26 - KA27 - KA28 (7,93 m + 7,59 m, am Bezugspunkt abgewickelt)

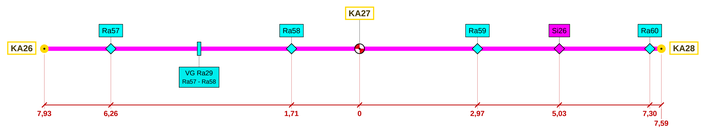

KA28 - KA29 - KA30 (7,88 m + 8,27 m, am Bezugspunkt abgewickelt)

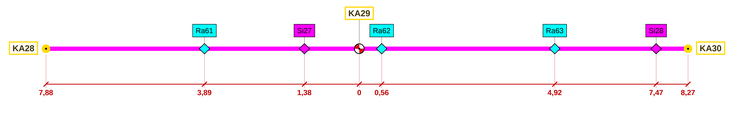

KA30 - KA31 - KA32 (8,42 m + 8,51 m, am Bezugspunkt abgewickelt)

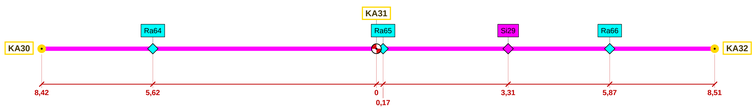


◆ Fluter (Farbe wie Plan) ▮ Vorschaltgerät (nur Lage) ⊘ Bezugspunkt (Messursprung) ○ Abschnittsende Maße [m] ab Bezugspunkt, rot


Blatt 4 · Bemaßung Innenring: Fluter ab jedem zweiten Ringpunkt (ab KI01, T-Stöße mitgezählt) bis zum nächsten gelben Punkt

Radsportzentrum Köln-Müngersdorf · Grundriss Dachkonstruktion · Beleuchtung Radbahn / Spielfläche · Maße in m, aus dem Grundriss (Blatt 1, 1:200) abgeleitet · Träger hier vergrößert dargestellt


KI20 - KI01 - KI02 (6,36 m + 6,34 m, am Bezugspunkt abgewickelt)

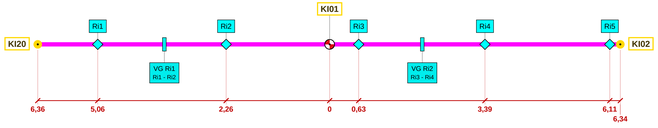


KI02 - KI03 - Q1-R (6,65 m + 2,35 m, am Bezugspunkt abgewickelt)

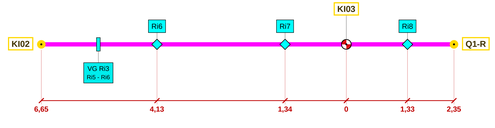


Q1-R - KI04 - KI05 (5,14 m + 6,69 m, am Bezugspunkt abgewickelt)

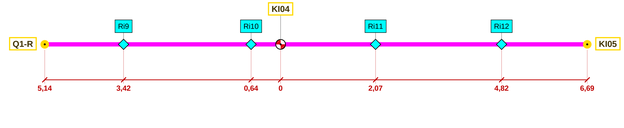

KI05 - Q3-R - Q4-R (15,25 m + 6,65 m, am Bezugspunkt abgewickelt)

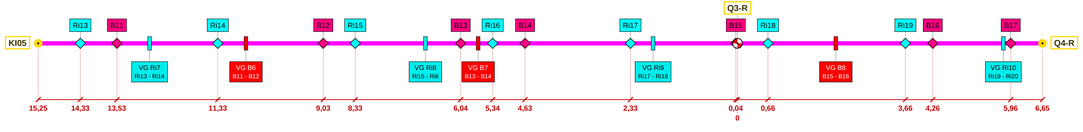


Q4-R - Q5-R - KI06 (6,71 m + 15,69 m, am Bezugspunkt abgewickelt)

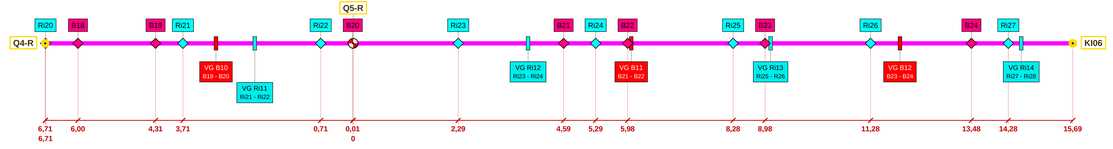


KI06 - KI07 - Q7-R (6,73 m + 4,72 m, am Bezugspunkt abgewickelt)


Q7-R - KI08 - KI09 (2,96 m + 6,47 m, am Bezugspunkt abgewickelt)

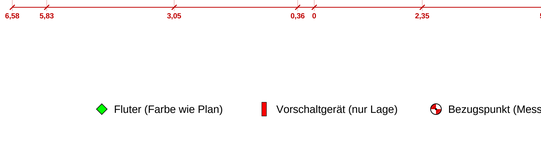


KI09 - KI10 - KI11 (6,53 m + 6,33 m, am Bezugspunkt abgewickelt)

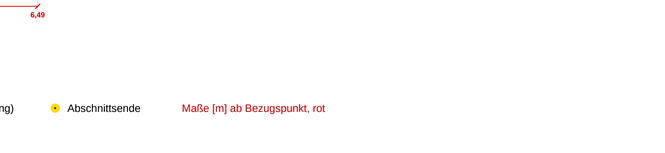


KI11 - KI12 - KI13 (6,42 m + 6,56 m, am Bezugspunkt abgewickelt)

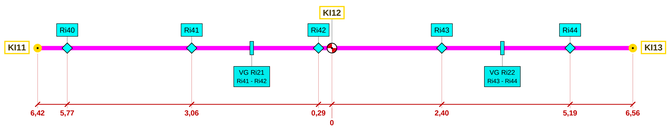


KI13 - Q7-L - KI14 (2,16 m + 5,19 m, am Bezugspunkt abgewickelt)

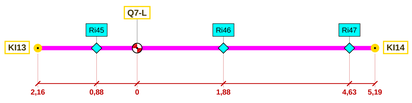


KI14 - KI15 - Q5-L (6,92 m + 15,13 m, am Bezugspunkt abgewickelt)

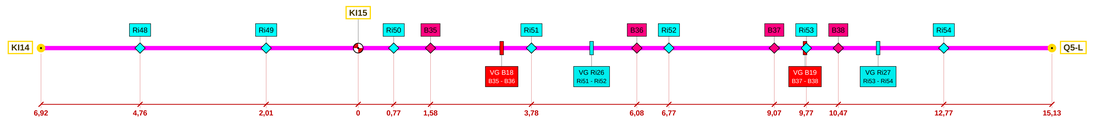


Q5-L - Q4-L - Q3-L (6,58 m + 6,65 m, am Bezugspunkt abgewickelt)

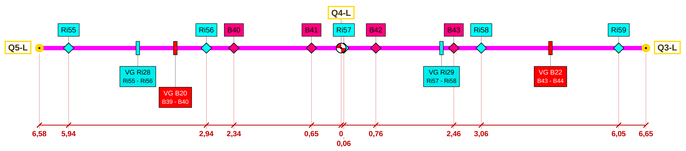


Q3-L - KI16 - KI17 (15,44 m + 7,20 m, am Bezugspunkt abgewickelt)

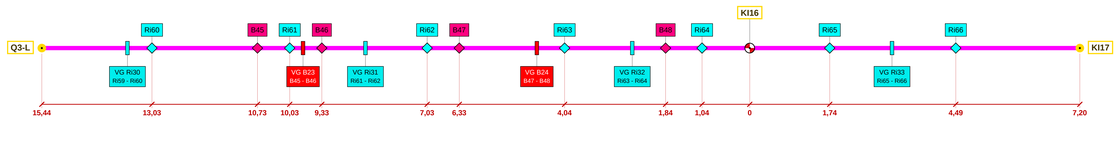

KI17 - Q1-L - KI18 (4,54 m + 2,90 m, am Bezugspunkt abgewickelt)

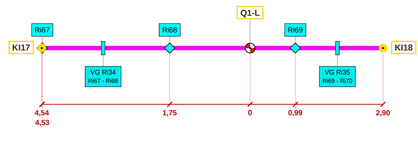

KI18 - KI19 - KI20 (6,58 m + 6,49 m, am Bezugspunkt abgewickelt)

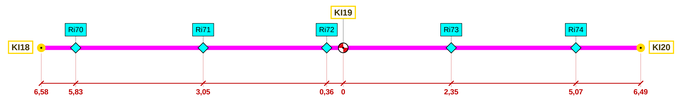

◆ Fluter (Farbe wie Plan) ▮ Vorschaltgerät (nur Lage) ◐ Bezugspunkt (Messursprung) ● Abschnittsende Maße [m] ab Bezugspunkt, rot