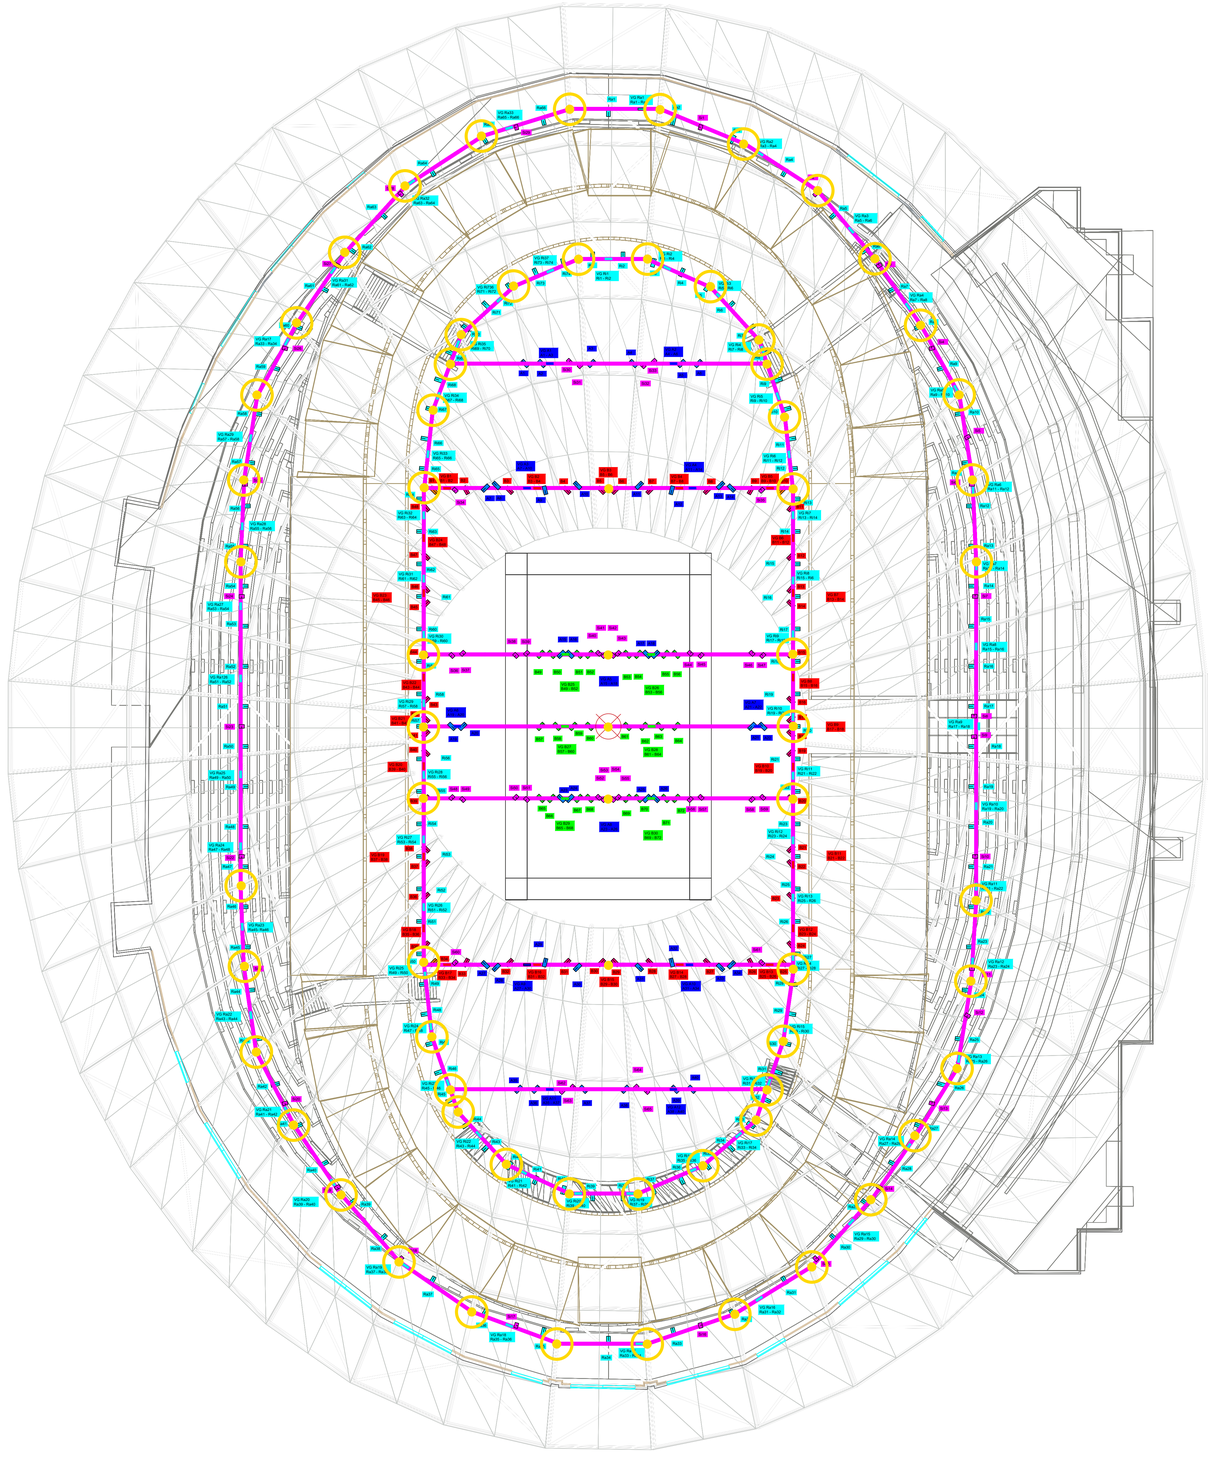


Beleuchtung

Ra1 - Ra66	LS 01 LED Fluter Sirius 1000W 5.000K
Ri1 - Ri74	LS 01 LED Fluter Sirius 1000W 5.000K
B1 - B48	LS 01.1 LED Fluter Sirius 1000W 5.700K
B48 - B72	LS 02 LED Fluter Sirius 500 5.700K
A1 - A40	LS 04 LED Fluter Sirius 500 5.000K
Si1 - Si65	LS 06 LED Fluter FL21 Mini 4.000K
VG Ra1 - VG Ra33	Vorschaltgerät LED Fluter Sirius 1000
VG Ri1 - VG Ri37	Vorschaltgerät LED Fluter Sirius 1000
VG B1 - VG B24	Vorschaltgerät LED Fluter Sirius 1000
VG B25 - VG B30	Vorschaltgerät LED Fluter Sirius 500
VG A1 - VG A12	Vorschaltgerät LED Fluter Sirius 500

Projekt:
RADSPORTZENTRUM KÖLN-MÜNGERSDORF
Peter-Günther-Weg | 50933 Köln-Müngersdorf
Gemarkung Müngersdorf | Flur 77 | Flurstücke 2205/0, 2206/0, 2207/0, 2208/0, 2210/0 tlw.

Bauherr:
Kölner Sportstätten GmbH
Aachener Straße 999 | 50933 Köln

Projektsteuerer:
moderne stadt
Brückenstraße 17 | 50667Köln | Tel: 0221-20594-33

Architekten Entwurfsplanung | Genehmigungsplanung | Ausführplanung LPH 5:
Schürmann Architekten
Schürbusch 26 | 48163 Münster | Tel. 0251-712450

Totalübernehmer:
Zech Sports GmbH
Heerdter Lohweg 35 | 40549 Düsseldorf | Tel. 0211-50664-300

Architekten Ausführungs- und Detailplanung LPH 5+:
arc | architektur concept Pfaffhausen + Kollegen
Scheringerstraße 3 |08056 Zwickau | Tel. 0375-27735-0

Ausführung Elektrotechnik:
Oertel & Prümm GmbH & Co.KG
Widdersdorferstraße 190 | 50825 Köln | Tel. 0221-546600

Planer Beleuchtung Radbahn / Spielfläche:
Siteco GmbH
Georg-Simon-Ohm-Straße 50 | 83301 Traunreut| Tel. 08669-33-0

Planinhalt:
Grundriss Dachkonstruktion
Beleuchtung Radbahn / Spielfläche

Bearbeiter:	Leistungsphase:	Blattformat:	Maßstab:	Datum Erstellung:
TS	Montageplanung	1950 x 841	1:50	21.08.2026

Projekt:	LPH:	Fachplaner:	Plantyp:	Ebene:	Planbereich:	Blattnr:	Status:	Index:
R S Z	008	L I C	G R	D A	2.1	0 0 1	P	0 1